УЧЕБНЫЙ КОМПЛЕКТ

Ведомость рабочих чертежей основного комплекта

Лист	Наименование	Примечание
1	Общие данные	
2	План сетей водоснабжения	
3	Профиль В1	

Ведомость основных комплектов рабочих чертежей

Обозначение	Наименование	Примечание
AI-TEST-01-HB	Наружные сети водоснабжения	

Ведомость ссылочных и прилагаемых документов

Обозначение	Наименование	Примечание
	Ссылочные документы	
ГОСТ Р 21.101-2026	Основные требования к проектной и рабочей документации	
ГОСТ 21.704-2011 (Изм. 1)	Рабочая документация наружных сетей водоснабжения и канализации	
ГОСТ 21.110-2013	Спецификация оборудования, изделий и материалов	
ГОСТ 21.206-2012	Условные обозначения трубопроводов	
ГОСТ 2.303-68	Линии	
ГОСТ 2.304-81	Шрифты чертежные	
	Прилагаемые документы	
AI-TEST-01-HB.CO	Спецификация оборудования, изделий и материалов	

Общие указания

Основанием для разработки является задание на проектирование.

Система координат условная, единицы — метры. Ось X направлена вправо, ось Y — вверх листа.

Проектируемая сеть В1 — подземный напорный водопровод из труб ПЭ 100 SDR 17 110×6,6. Длина трассы — 360,00 м.

Длина трубы в спецификации принята по оси трассы без запаса.

В исходных данных заданы отметки оси трубопровода; на профиле показаны отметки низа трубы (ось минус половина наружного диаметра). Труба показана сплошной толстой линией.

Принятые допущения и ограничения приведены в отчёте о проверках.

Принятые допущения


В1 назначено условно. Отметка земли принята проектной. Натурная поверхность не задана.

Материал и SDR отводов приняты как у трубы. Для учебного профиля принято отсутствие изоляции; основание не задано.

Пропуски отметок не интерполируются. Полный перечень оговорок дан в отчёте о проверках.

						AI-TEST-01-HB		
						Учебный участок водопровода		
Изм.	Кол.уч.	Лист	№ док.	Подп.	Дата			
Разраб.						Общие данные	Стадия	Лист	Листов
Пров.							Р	1	3
Н. контр.									
ГИП									

Формат А3

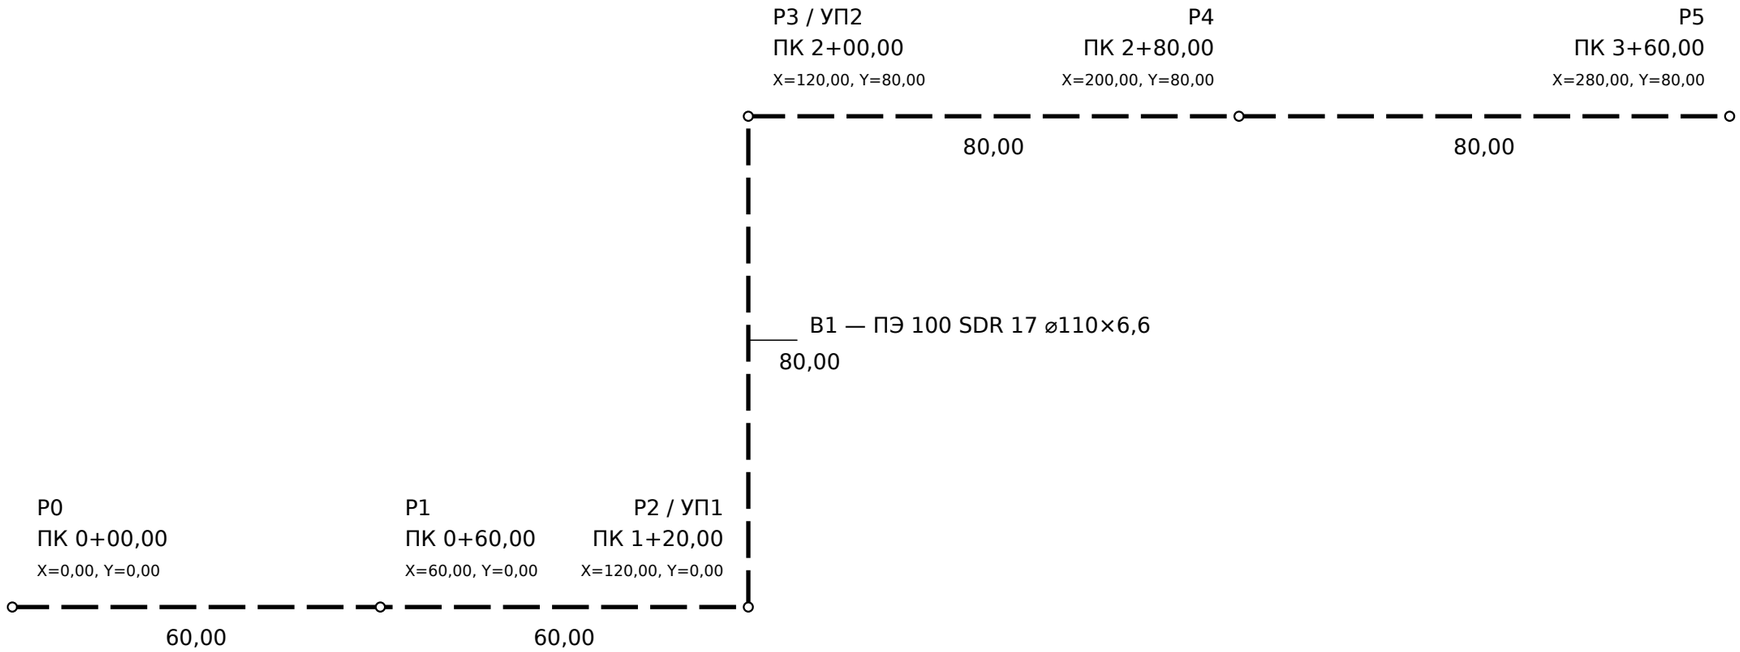

Условные обозначения

— — — · — В1 — проектируемый подземный водопровод

— — ┘ — УП — угол поворота, отвод

Р0…Pn — Характерные точки трассы

						AI-TEST-01-НВ
						Учебный участок водопровода
Изм.	Кол.уч.	Лист	№ док.	Подп.	Дата	
Разраб.						План сетей водоснабжения (1:1000)
Пров.						Стадия: Р; Лист: 2; Листов:
Н. контр.						
ГИП						


Формат А3

УЧЕБНЫЙ КОМПЛЕКТ

М 1:2000 по горизонтали

М 1:100 по вертикали

УГ 98,17

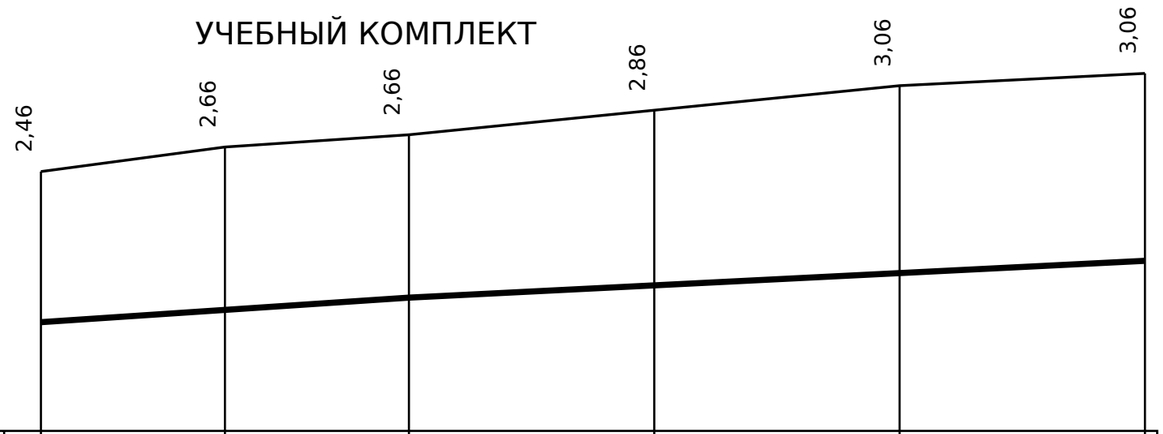

Проектная отметка низа трубы или низа лотка колодца, м	99,95	100,15	100,35	100,55	100,75	100,95
Проектная отметка земли, м	102,40	102,80	103,00	103,40	103,80	104,00
Натурная отметка земли, м	—	—	—	—	—	—
Обозначение трубы и тип изоляции	В1 — Труба ПЭ 100 SDR 17 ⌀110×6,6 Без изоляции					
Основание						
Уклон, ‰; длина, м	3,33 / 60,00	3,33 / 60,00	2,50 / 80,00	2,50 / 80,00	2,50 / 80,00	
Расстояние, м		60,00	60,00	80,00	80,00	80,00
Номер колодца, точки, угла поворота	Р0	Р1	Р2 / УП1	Р3 / УП2	Р4	Р5
Пикеты	ПК 0+00,00	ПК 0+60,00	ПК 1+20,00	ПК 2+00,00	ПК 2+80,00	ПК 3+60,00

Изм.	Кол.уч.	Лист	№ док.	Подп.	Дата
Разраб.					
Пров.					
Н. контр.					
ГИП					

AI-TEST-01-НВ

Учебный участок водопровода

Профиль В1	Стадия	Лист	Листов
	Р	3	

Формат А3

УЧЕБНЫЙ КОМПЛЕКТ

Поз.	Наименование и техническая характеристика	Тип, марка, обозначение документа, опросного листа	Код продукции	Поставщик	Ед. измерения	Коли-чество	Масса 1 ед., кг	Примечание
1	Отвод 90° ПЭ 100 SDR 17 110				шт.	2		Материал и SDR приняты как у трубы
2	Труба ПЭ 100 SDR 17 110×6,6				м	360,00		Без запаса и вычета монтажных длин отводов

Изм.	Кол.уч.	Лист	№ док.	Подп.	Дата
Разраб.					
Пров.					
Н. контр.					
ГИП					

AI-TEST-01-HB.CO

Учебный участок водопровода

Спецификация оборудования, изделий и материалов	Стадия	Лист	Листов
	Р		1

Формат А3