УЧЕБНЫЙ КОМПЛЕКТ

М 1:2000 по горизонтали

М 1:100 по вертикали

УГ 98,17

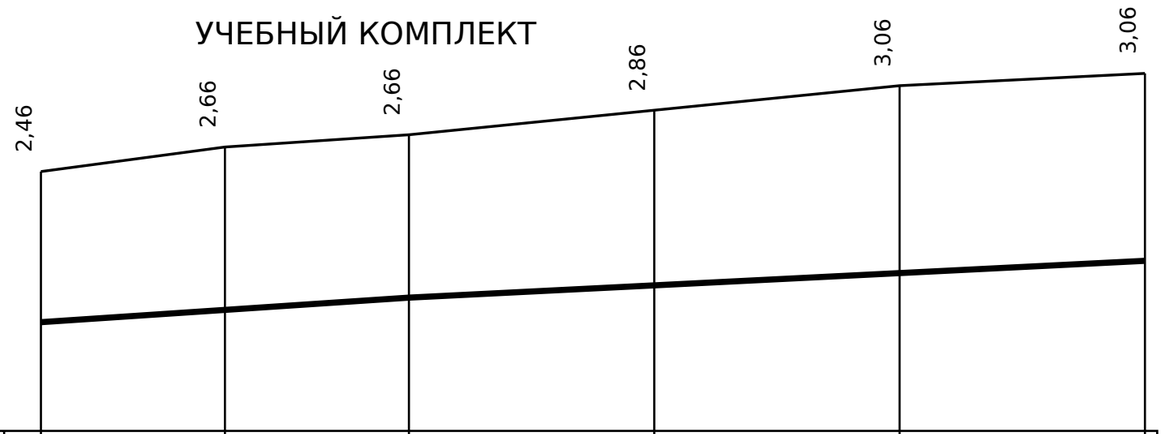

Проектная отметка низа трубы или низа лотка колодца, м	99,95	100,15	100,35	100,55	100,75	100,95
Проектная отметка земли, м	102,40	102,80	103,00	103,40	103,80	104,00
Натурная отметка земли, м	—	—	—	—	—	—
Обозначение трубы и тип изоляции	В1 — Труба ПЭ 100 SDR 17 ⌀110×6,6 Без изоляции					
Основание						
Уклон, ‰; длина, м	3,33 / 60,00	3,33 / 60,00	2,50 / 80,00	2,50 / 80,00	2,50 / 80,00	
Расстояние, м		60,00	60,00	80,00	80,00	80,00
Номер колодца, точки, угла поворота	Р0	Р1	Р2 / УП1	Р3 / УП2	Р4	Р5
Пикеты	ПК 0+00,00	ПК 0+60,00	ПК 1+20,00	ПК 2+00,00	ПК 2+80,00	ПК 3+60,00

Изм.	Кол.уч.	Лист	№ док.	Подп.	Дата
Разраб.					
Пров.					
Н. контр.					
ГИП					

AI-TEST-01-НВ

Учебный участок водопровода

Профиль В1	Стадия	Лист	Листов
	Р	3	

Формат А3