УЧЕБНЫЙ КОМПЛЕКТ

М 1:2000 по горизонтали

М 1:100 по вертикали

УГ 98,17

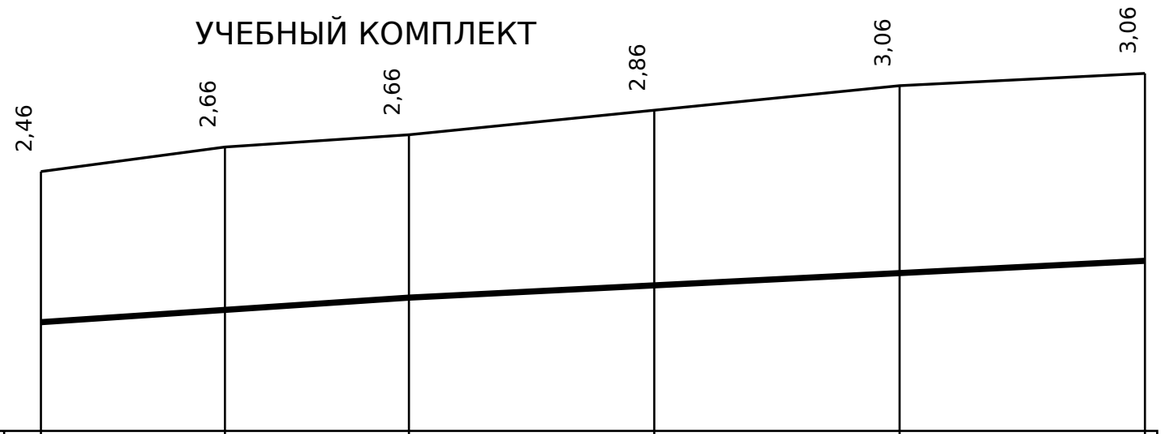


| | | | | | | |
|---|---|---|---|---|---|---|
| Проектная отметка низа трубы или низа лотка колодца, м | 99,95 | 100,15 | 100,35 | 100,55 | 100,75 | 100,95 |
| Проектная отметка земли, м | 102,40 | 102,80 | 103,00 | 103,40 | 103,80 | 104,00 |
| Натурная отметка земли, м | — | — | — | — | — | — |
| Обозначение трубы и тип изоляции | В1 — Труба ПЭ 100 SDR 17 ⌀110×6,6 Без изоляции | | | | | |
| Основание | | | | | | |
| Уклон, ‰; длина, м | 3,33 / 60,00 | 3,33 / 60,00 | 2,50 / 80,00 | 2,50 / 80,00 | 2,50 / 80,00 | |
| Расстояние, м | | 60,00 | 60,00 | 80,00 | 80,00 | 80,00 |
| Номер колодца, точки, угла поворота | Р0 | Р1 | Р2 / УП1 | Р3 / УП2 | Р4 | Р5 |
| Пикеты | ПК 0+00,00 | ПК 0+60,00 | ПК 1+20,00 | ПК 2+00,00 | ПК 2+80,00 | ПК 3+60,00 |

| Изм. | Кол.уч. | Лист | № док. | Подп. | Дата |
|---|---|---|---|---|---|
| Разраб. | | | | | |
| Пров. | | | | | |
| | | | | | |
| | | | | | |
| Н. контр. | | | | | |
| ГИП | | | | | |

AI-TEST-01-НВ

Учебный участок водопровода

| Профиль В1 | Стадия | Лист | Листов |
|---|---|---|---|
| | Р | 3 | |

Формат А3