Масштаб:

по горизонтали 1:2000

по вертикали 1:100

УГ 99,45

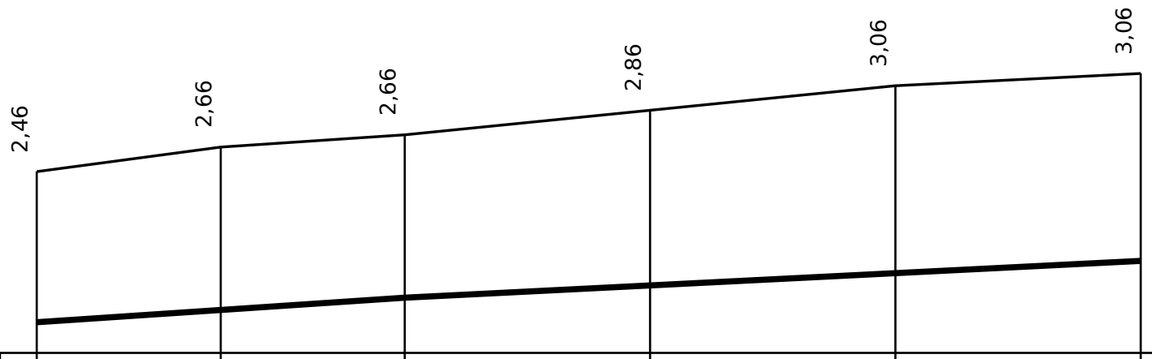

Проектная отметка низа трубы или низа лотка колодца, м	99,95	100,15	100,35	100,55	100,75	100,95	
Проектная отметка земли, м	102,40	102,80	103,00	103,40	103,80	104,00	
Натурная отметка земли, м	—	—	—	—	—	—	
Обозначение трубы и тип изоляции	Труба полиэтиленовая ПЭ 100 SDR 17 ⌀110×6,6 Без изоляции						
Основание							
Уклон, ‰; длина, м	3,3 / 60,00	3,3 / 60,00	2,5 / 80,00	2,5 / 80,00	2,5 / 80,00		
Расстояние, м		60,00	60,00	80,00	80,00	80,00	
Номер колодца, точки, угла поворота	Р0	Р1	Р2 / УП1	Р3 / УП2	Р4	Р5	
Пикеты	ПК 0+00,00	ПК 0+60,00	ПК 1+20,00	ПК 2+00,00	ПК 2+80,00	ПК 3+60,00	

Изм.	Кол.уч.	Лист	№ док.	Подп.	Дата
Разраб.					
Пров.					
Н. контр.					
ГИП					

AI-TEST-01-НВ

Учебный участок водопровода

Профиль В1	Стадия	Лист	Листов
	Р	3	

Формат А3